


舗装縦断図

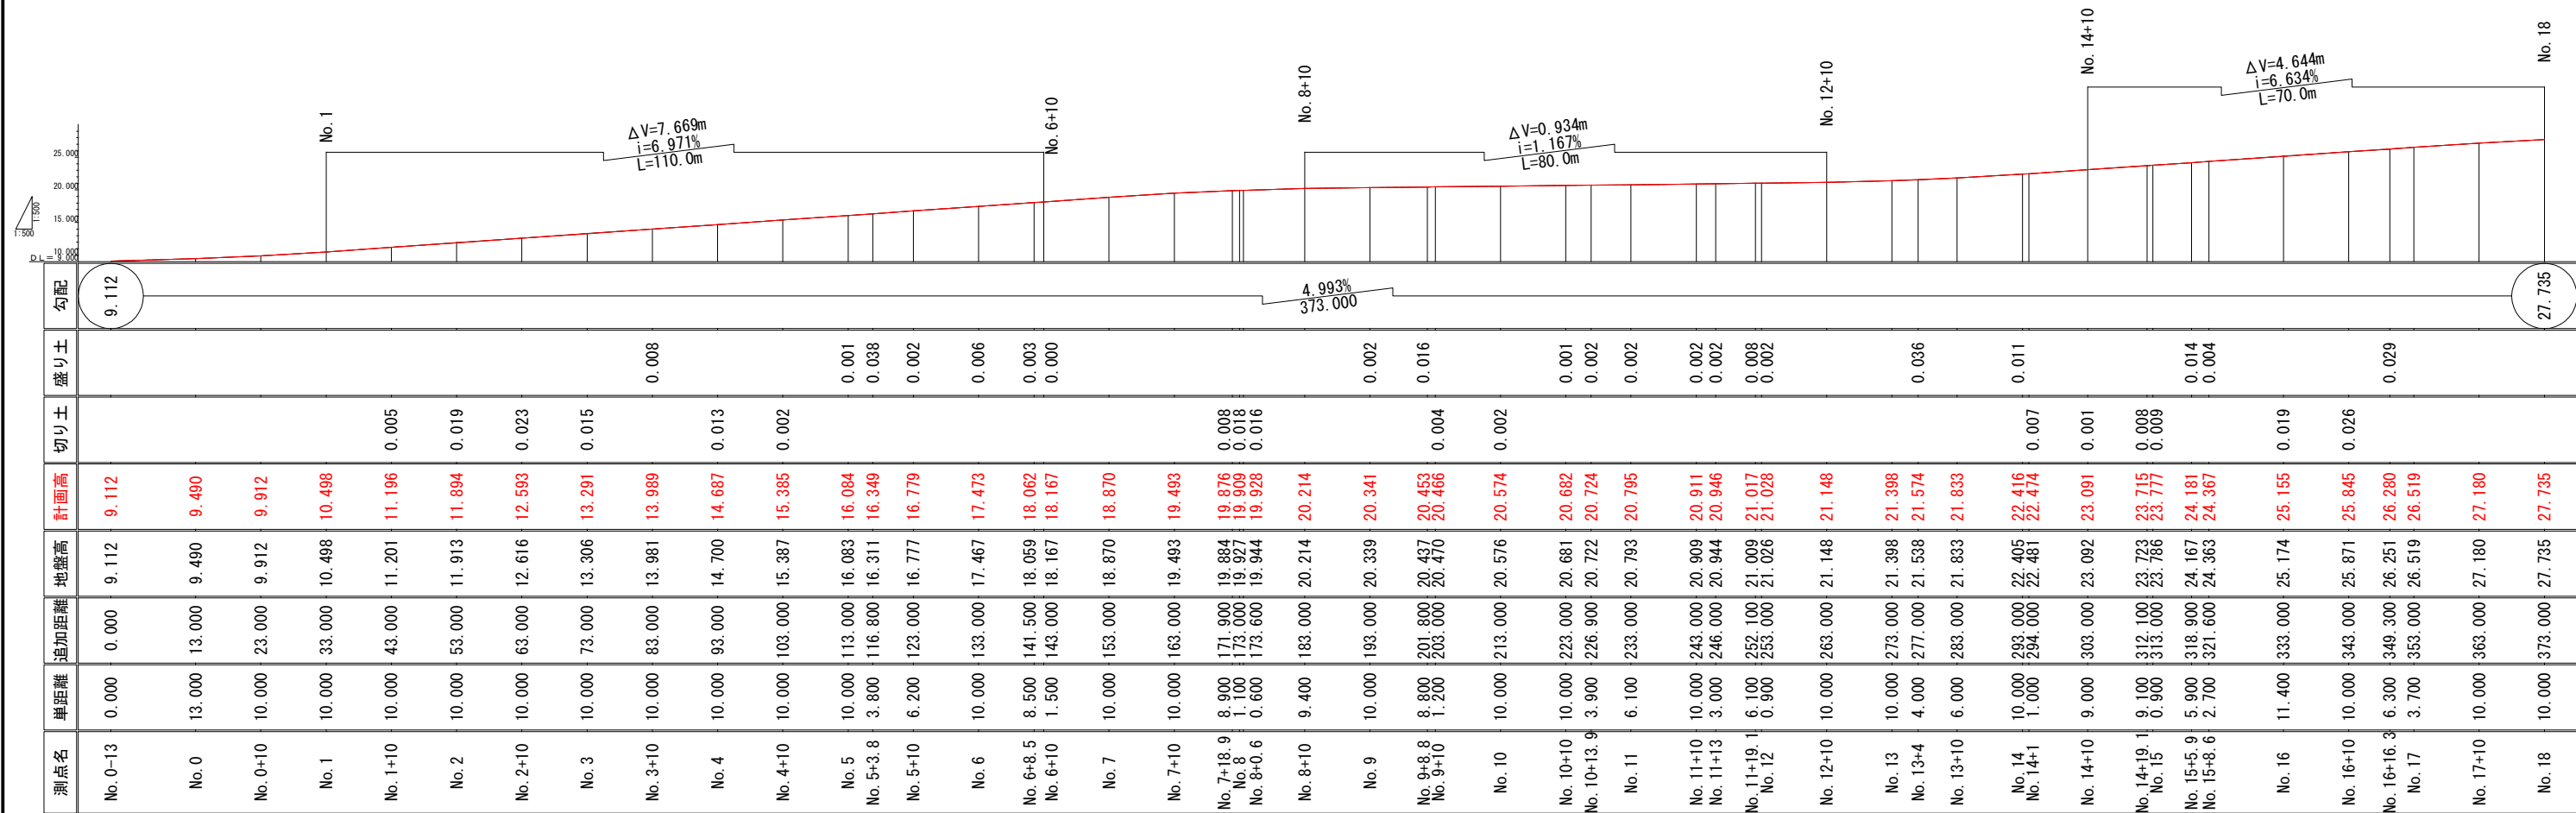

工 事 名	市道 上古賀大和第1号線舗装打換工事		
図 面 名	舗 装 縦 断 図		
路 線 名	市道 上古賀大和第1号線		
作 成 日	2025 年 8 月 19 日		
縮 尺	1/500 (A1)	図面番号	1/1
施 工 者	有限会社 三雄建設		